

PT. PLN (PERSERO) UNIT PELAKSANA TRANSMISI MALANG
Jl. Raya Karanglo No.90, Banjararum, Kec. Singosari, Kabupaten Malang,
Jawa Timur 65153, Indonesia



PEKERJAAN
PEMBANGUNAN DAN PERBAIKAN SARANA GRAVEL DAN OIL PIT
Jl. Raya Karanglo No.90, Kabupaten Malang, Jawa Timur

DIKERJAKAN OLEH :
PT. AMSAK BANGUN PERSADA
Ruko Golden Boulevard Blok E 09, BSD City, Kec. Tangerang, Jl. Pahlawan Seribu, Lengkong Karya, Serpong Utara, Tangerang Selatan, Kota Tangerang, Banten, 15320


	
PT PLN (PERSERO) UPT JBM UPT MALANG DOCUMENT APPROVAL	
☒ No exception noted	Tanggal 15/10/25
☐ Exception noted	Tanda Tangan
☐ Return For Correction	




LIST DRAWING

NO.	LIST GAMBAR	HALAMAN
1	Daftar Isi	1
2	Drawing Oil Pit Gardu induk Kebon Agung	2
3	Detail Gravel Dan Kanstin Gardu induk Kebon Agung	3
4	Lay Out Gravel Gardu induk Kebon Agung	4


 PT PLN (PERSERO) UIT JBM UPT MALANG DOCUMENT APPROVAL	
☒ No exception noted ☐ Exception noted ☐ Return For Correction	Tanggal 15/10/25 Tanda Tangan 

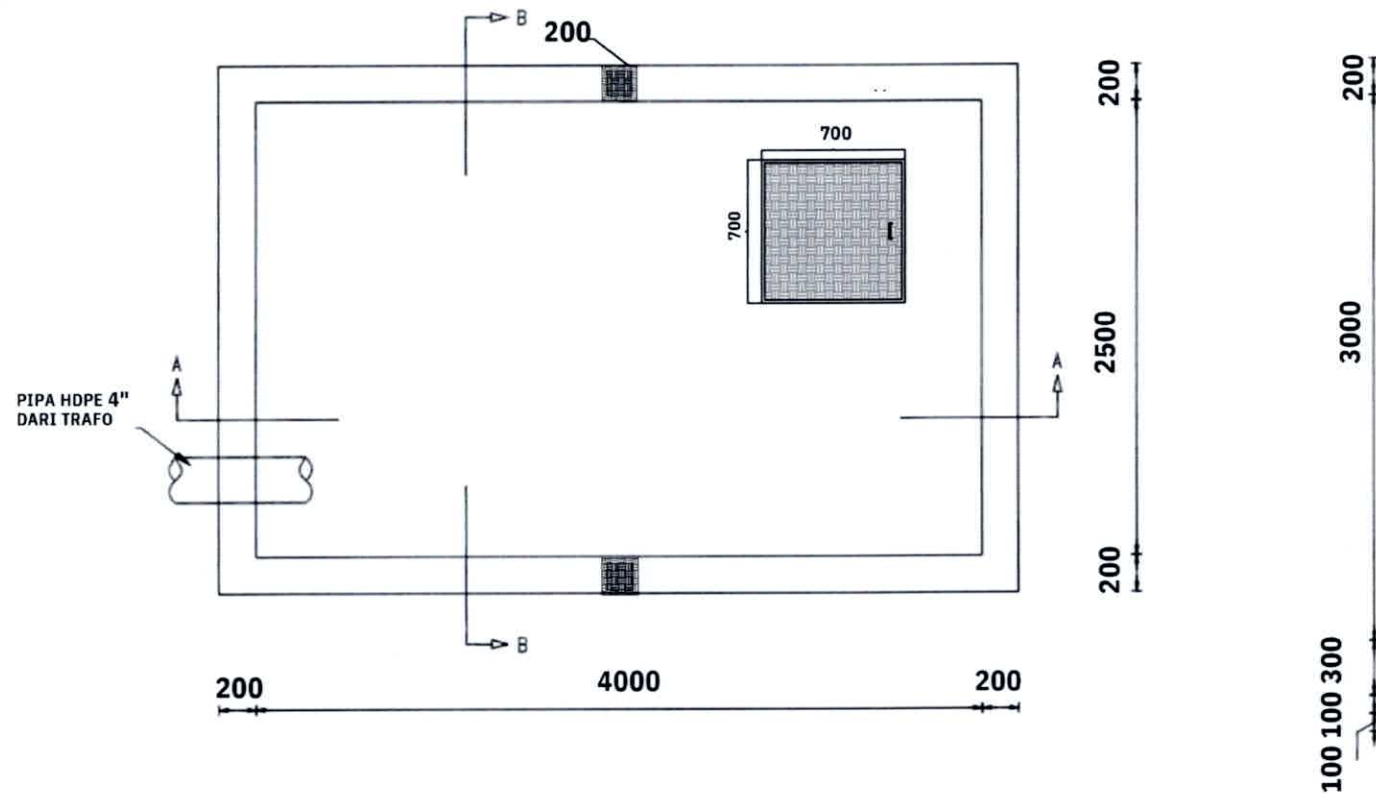


TOP VIEW

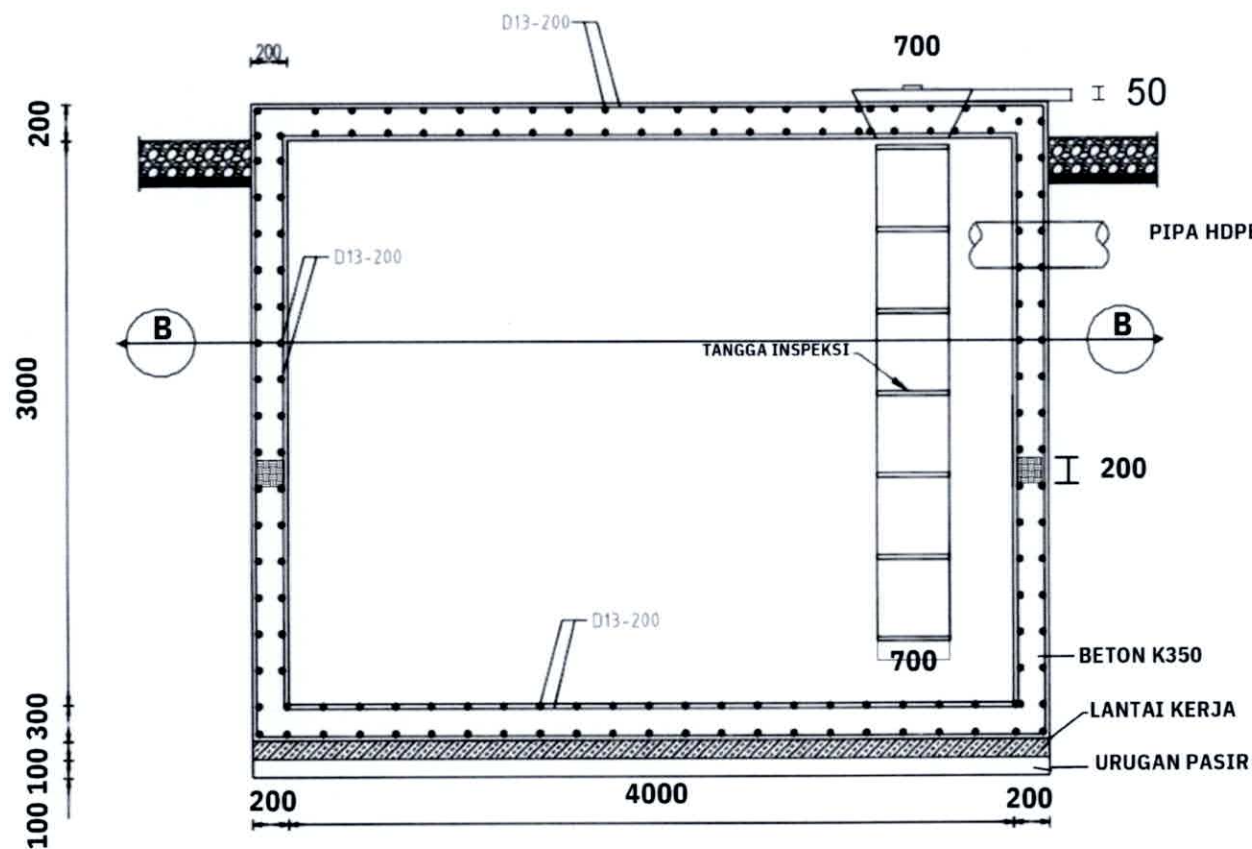

POTONGAN A-A

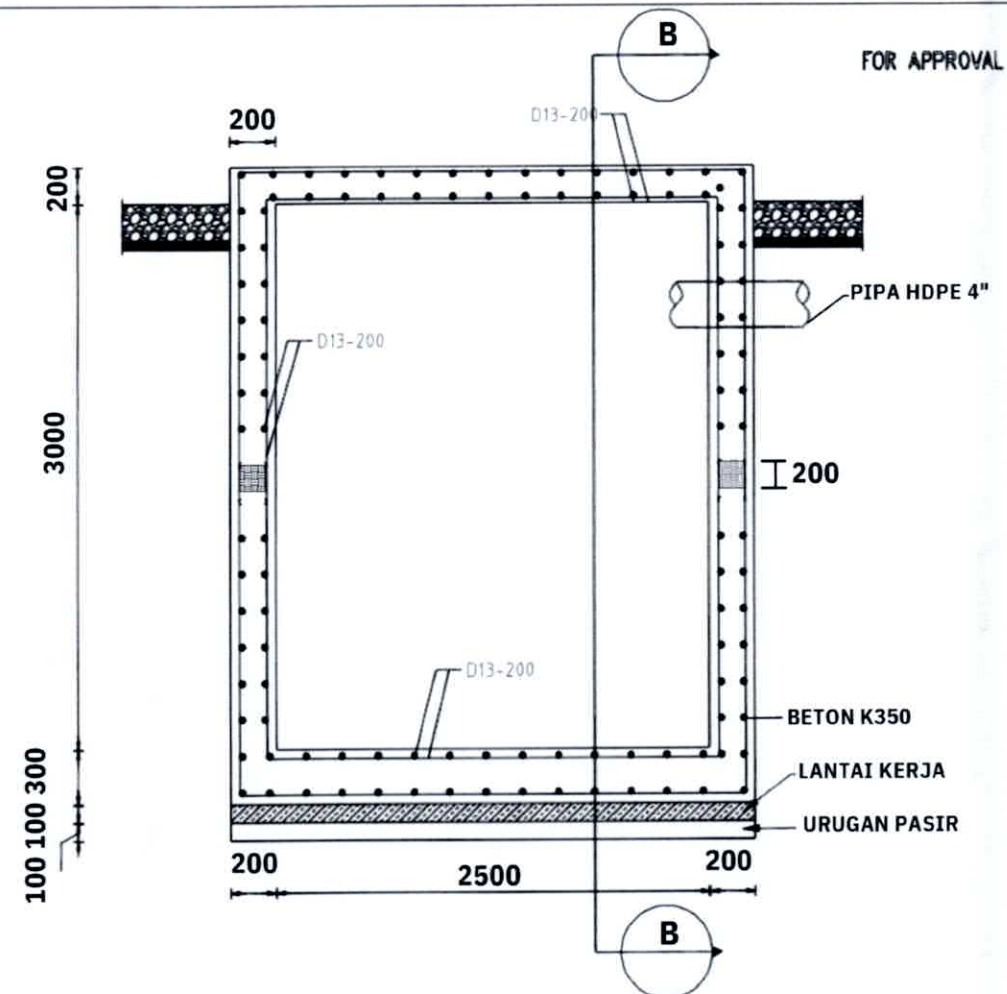


POTONGAN B-B

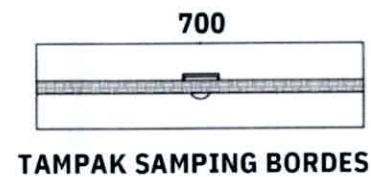

TAMPAK SAMPING BORDES

DETAIL BORDES	
TEBAL BORDES	700 X 700
SIKU	50
BALOK TENGAH	200 x 200

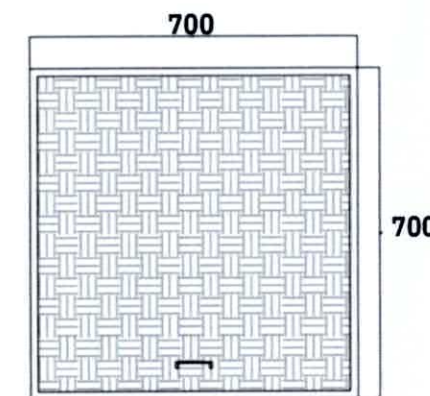

TAMPAK ATAS BORDES

FOR APPROVAL

CATATAN :

1. SEMUA DIMENSI DALAM SATUAN Milimeter (KECUALI ADA KETERANGAN LAIN)
2. ELEVASI DALAM SATUAN METER, DARI ± 0.00

PT PLN (PERSERO) UIT JBM UPT MALANG DOCUMENT APPROVAL	
☒ No exception noted	Tanggal 15/10/25
☐ Exception noted	Tanda Tangan
☐ Return For Correction	



PT. PLN (PERSERO) UIT JBM
UNIT PELAKSANA TRANSMISI
MALANG

CONTRACT :

PROJECT :

Pembangunan dan Perbaikan Sarana
Gravel dan Oil UPT Malang

PROJECT :

PT. AMSAK BANGUN PERSADA

TITLE :

DETAIL OIL PIT
Gardu Induk Kebon Agung

DRAW & DESIGNS	CHECKED	APPROVED
		ASMAN RENEY
DATE : 30/09/2025	PAGE : 2/4	REV : 1
SCALE : MTS		

FOR APPROVAL

CATATAN :

1. SEMUA DIMENSI DALAM SATUAN CENTIMETER (KECUALI ADA KETERANGAN LAIN)
2. ELEVASI DALAM SATUAN METER, DARI ±0.00

* Tambahkan plastik 80 micron diatas pasir.



PT. PLN (PERSERO) UIT JBM
UNIT PELAKSANA TRANSMISI
MALANG

CONTRACT :

PROJECT :

Pembangunan dan Perbaikan Sarana
Gravel dan Oil UPT Malang


PROJECT :

PT. AMSAK BANGUN PERSADA

TITLE :

DETAIL GRAVEL DAN KANSTAIN

DRAW & DESIGNS	CHECKED	APPROVED
		ASMAN REDEV
DATE : 06/06/2025	PAGE : 3/4	REV : 1
SCALE : NTS		

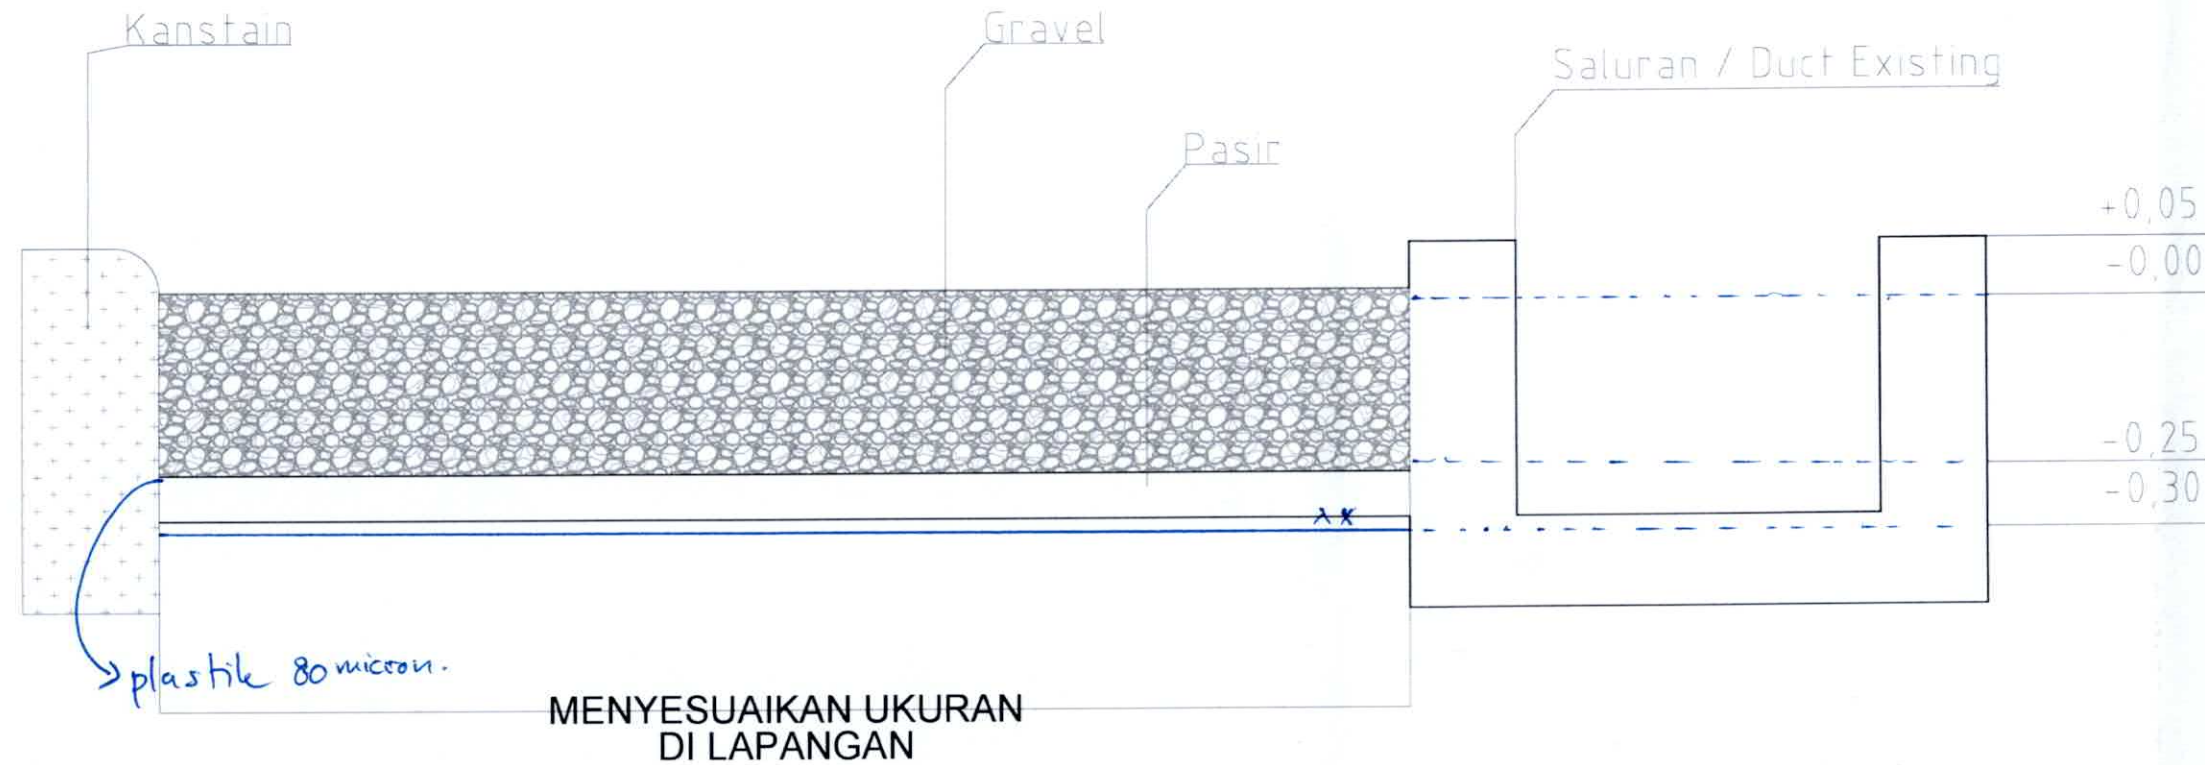

PT PLN (PERSERO) UIT JBM
UPT MALANG
DOCUMENT APPROVAL


☐ No exception noted

☒ Exception noted

☐ Return For Correction


Tanggal 15/10 '25

Tanda Tangan

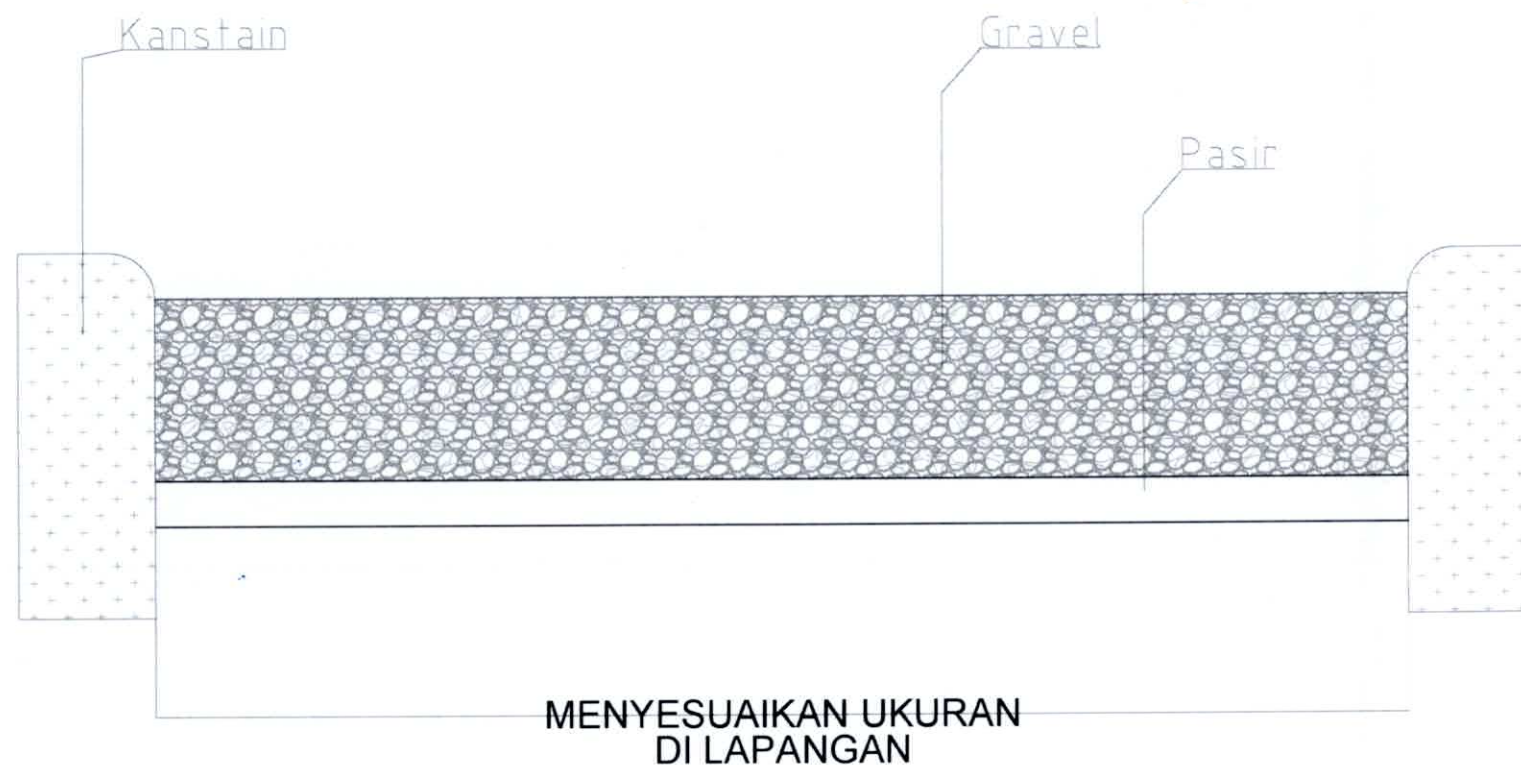

FOR APPROVAL

 PT PLN (PERSERO) UIT JBM UPT MALANG DOCUMENT APPROVAL	
☒ No exception noted ☐ Exception noted ☐ Return For Correction	Tanggal 15/10/25 Tanda Tangan 

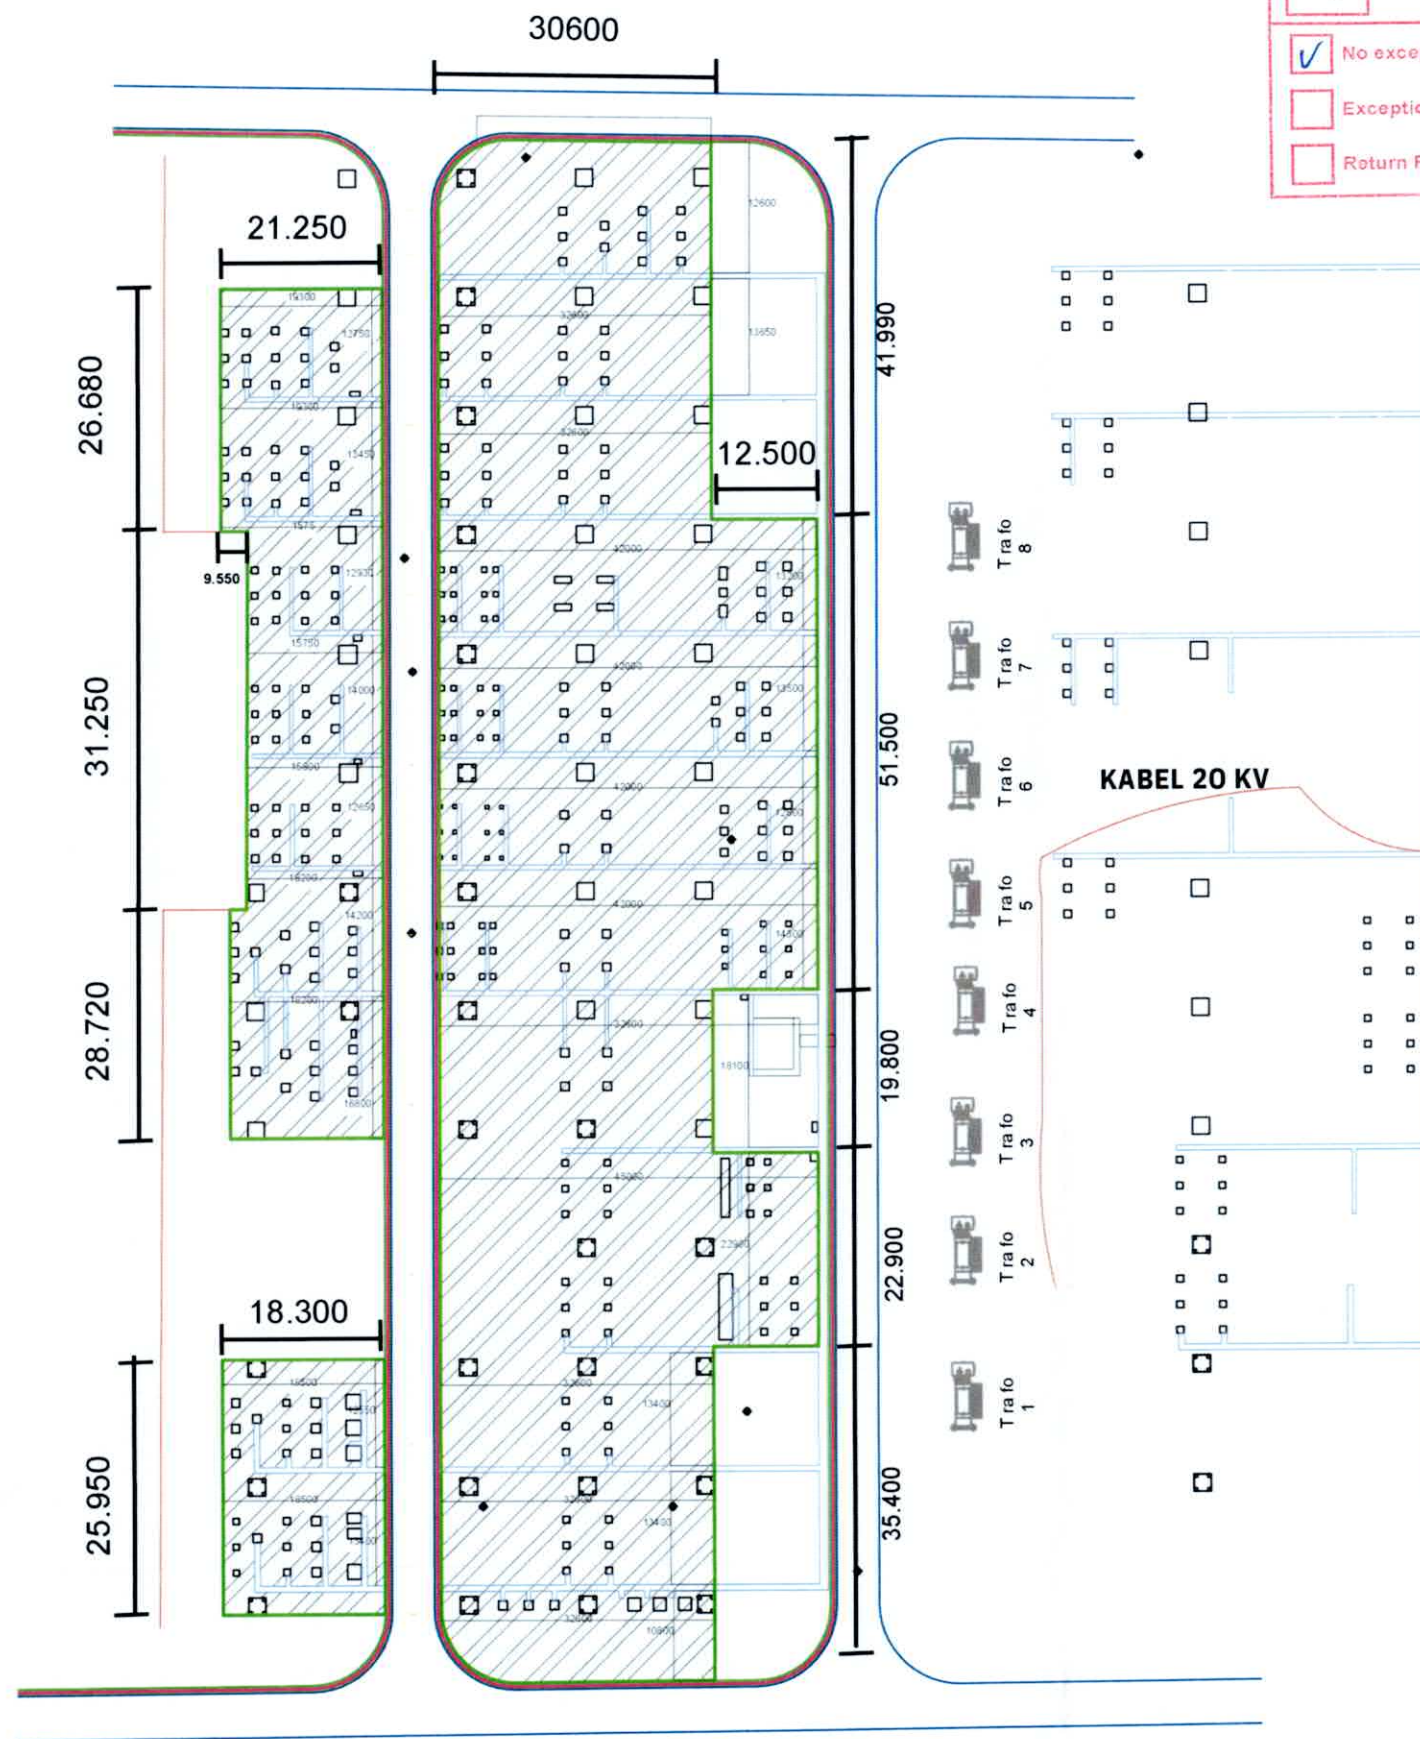

CATATAN :

1. SEMUA DIMENSI DALAM SATUAN Milimeter (KECUALI ADA KETERANGAN LAIN)
2. ELEVASI DALAM SATUAN METER, DARI ±0.00

 PT. PLN (PERSERO) UIT JBM UNIT PELAKSANA TRANSMISI MALANG		
CONTRACT :		
PROJECT : Pembangunan dan Perbaikan Sarana Gravel dan Oil UPT Malang		
PROJECT : PT. AMSAK BANGUN PERSADA		
TITLE : Layout Gravel Gardu Induk Kebon Agung		
DRAW & DESIGNS	CHECKED	APPROVED
		ASMAN REVEV
DATE : 30/09/2025		PAGE : 4/4
SCALE : NTS		REV : 1